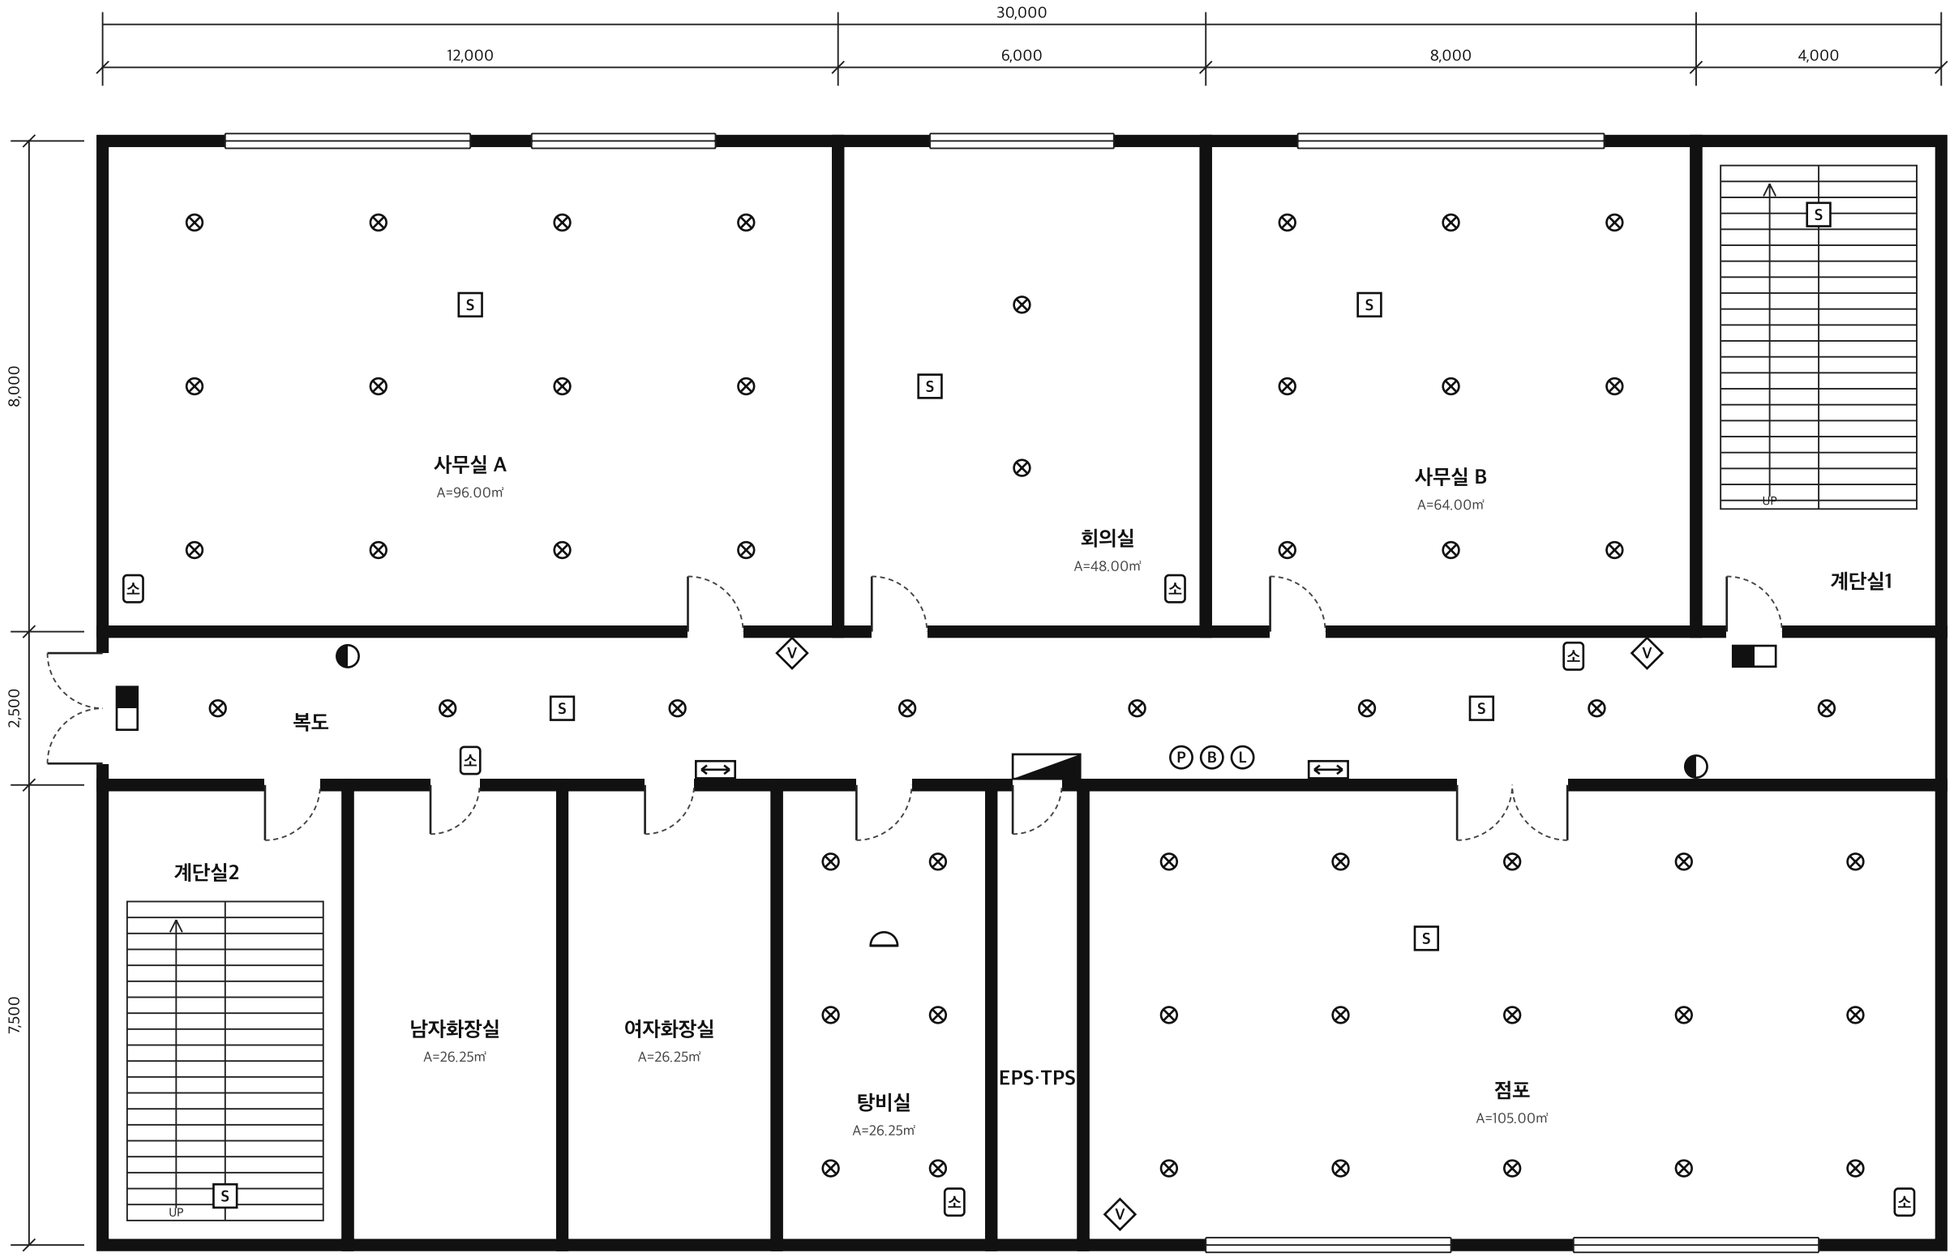


범 례

- 소화기 (분말 3.3kg)
- 옥내소화전함
- 간이스프링클러헤드 (하향식)
- 연기감지기 (광전식 2종)
- 열감지기 (차동식 스포트형 2종)
- 발신기
- 경종
- 표시등
- 시각경보기
- 수신기 (P형)
- 피난구유도등
- 통로유도등
- 비상조명등

3층 소방설비 평면도

SCALE : 1/100

공 사 명	성수동 근린생활시설 신축공사
도 면 명	3층 소방설비 평면도
축 척	1/100 (A3)
도면번호	FP-103
일 자	2026. 11.
설 계	PlanWise 샘플